

I-501 Kitchen Coordination Candidate

厨房平面与立面协调候选

Status: CANDIDATE / NOT FOR CONSTRUCTION

Existing objects: 70

IFC SHA: 7a50b87e8f48a7c2...

Overlay = world bbox coordination envelope

NOT fabrication / opening / rough-in dimensions

- Cabinet x1
- 厨房移门门垛墙 x1
- HD01 x1
- OV01 x1
- WD01 x1
- BD600DW x2
- BD600P x2
- BN1200 x1
- BN450 x1
- BN900 x1
- BNW900C x1
- BS1200P x2
- BW1200 x1
- BW450 x1
- BW900 x2
- CAB-A x1
- D600P x4
- FRE01 x1
- FRE02 x1
- FRI01 x1
- FRI02 x1
- H08 x1
- H09 x1
- HC01 x1
- HC02 x1
- HD1200 x2
- HD450 x3
- HD600 x8
- HD900 x3
- HL x1
- HP x1
- Libelle x1
- PAN01 x1
- POT1200 x1
- POT600 x1
- SB01 x1
- SB02 x1
- SB03 x2
- SIS04 x1
- SKI03 x1
- SKI04 x2
- VVD Island Inner Sideboard x1
- VVD Island worktop board x1
- W06L x1
- FAU01 x1
- SIN01 x1
- CHA01 x2
- TAB01 x1

PRODUCT INTERFACES · NO PROJECT XYZ

APP-009 · SJ85ZX26MC · CANDIDATE / NOT PURCHASED

Use: 西厨岛台 · G3/4 cold water · drain Ø38 mm

APP-010 · SJ85ZX26MC · CANDIDATE / NOT PURCHASED

Use: 西厨岛台 · G3/4 cold water · drain Ø38 mm

Niche H780–835 mm · W600–608 mm · D≥550 mm (official product constraint)


BLOCK: rough-in XYZ / valves / hose path / opening position

BLOCK INT1-BLOCK-001: equipment_installation_drawings

BLOCK INT1-BLOCK-002: gas_meter_site_survey

BLOCK INT1-BLOCK-003: sanitary_rough_in_drawings

BLOCK INT1-BLOCK-004: hardware_motion_envelopes

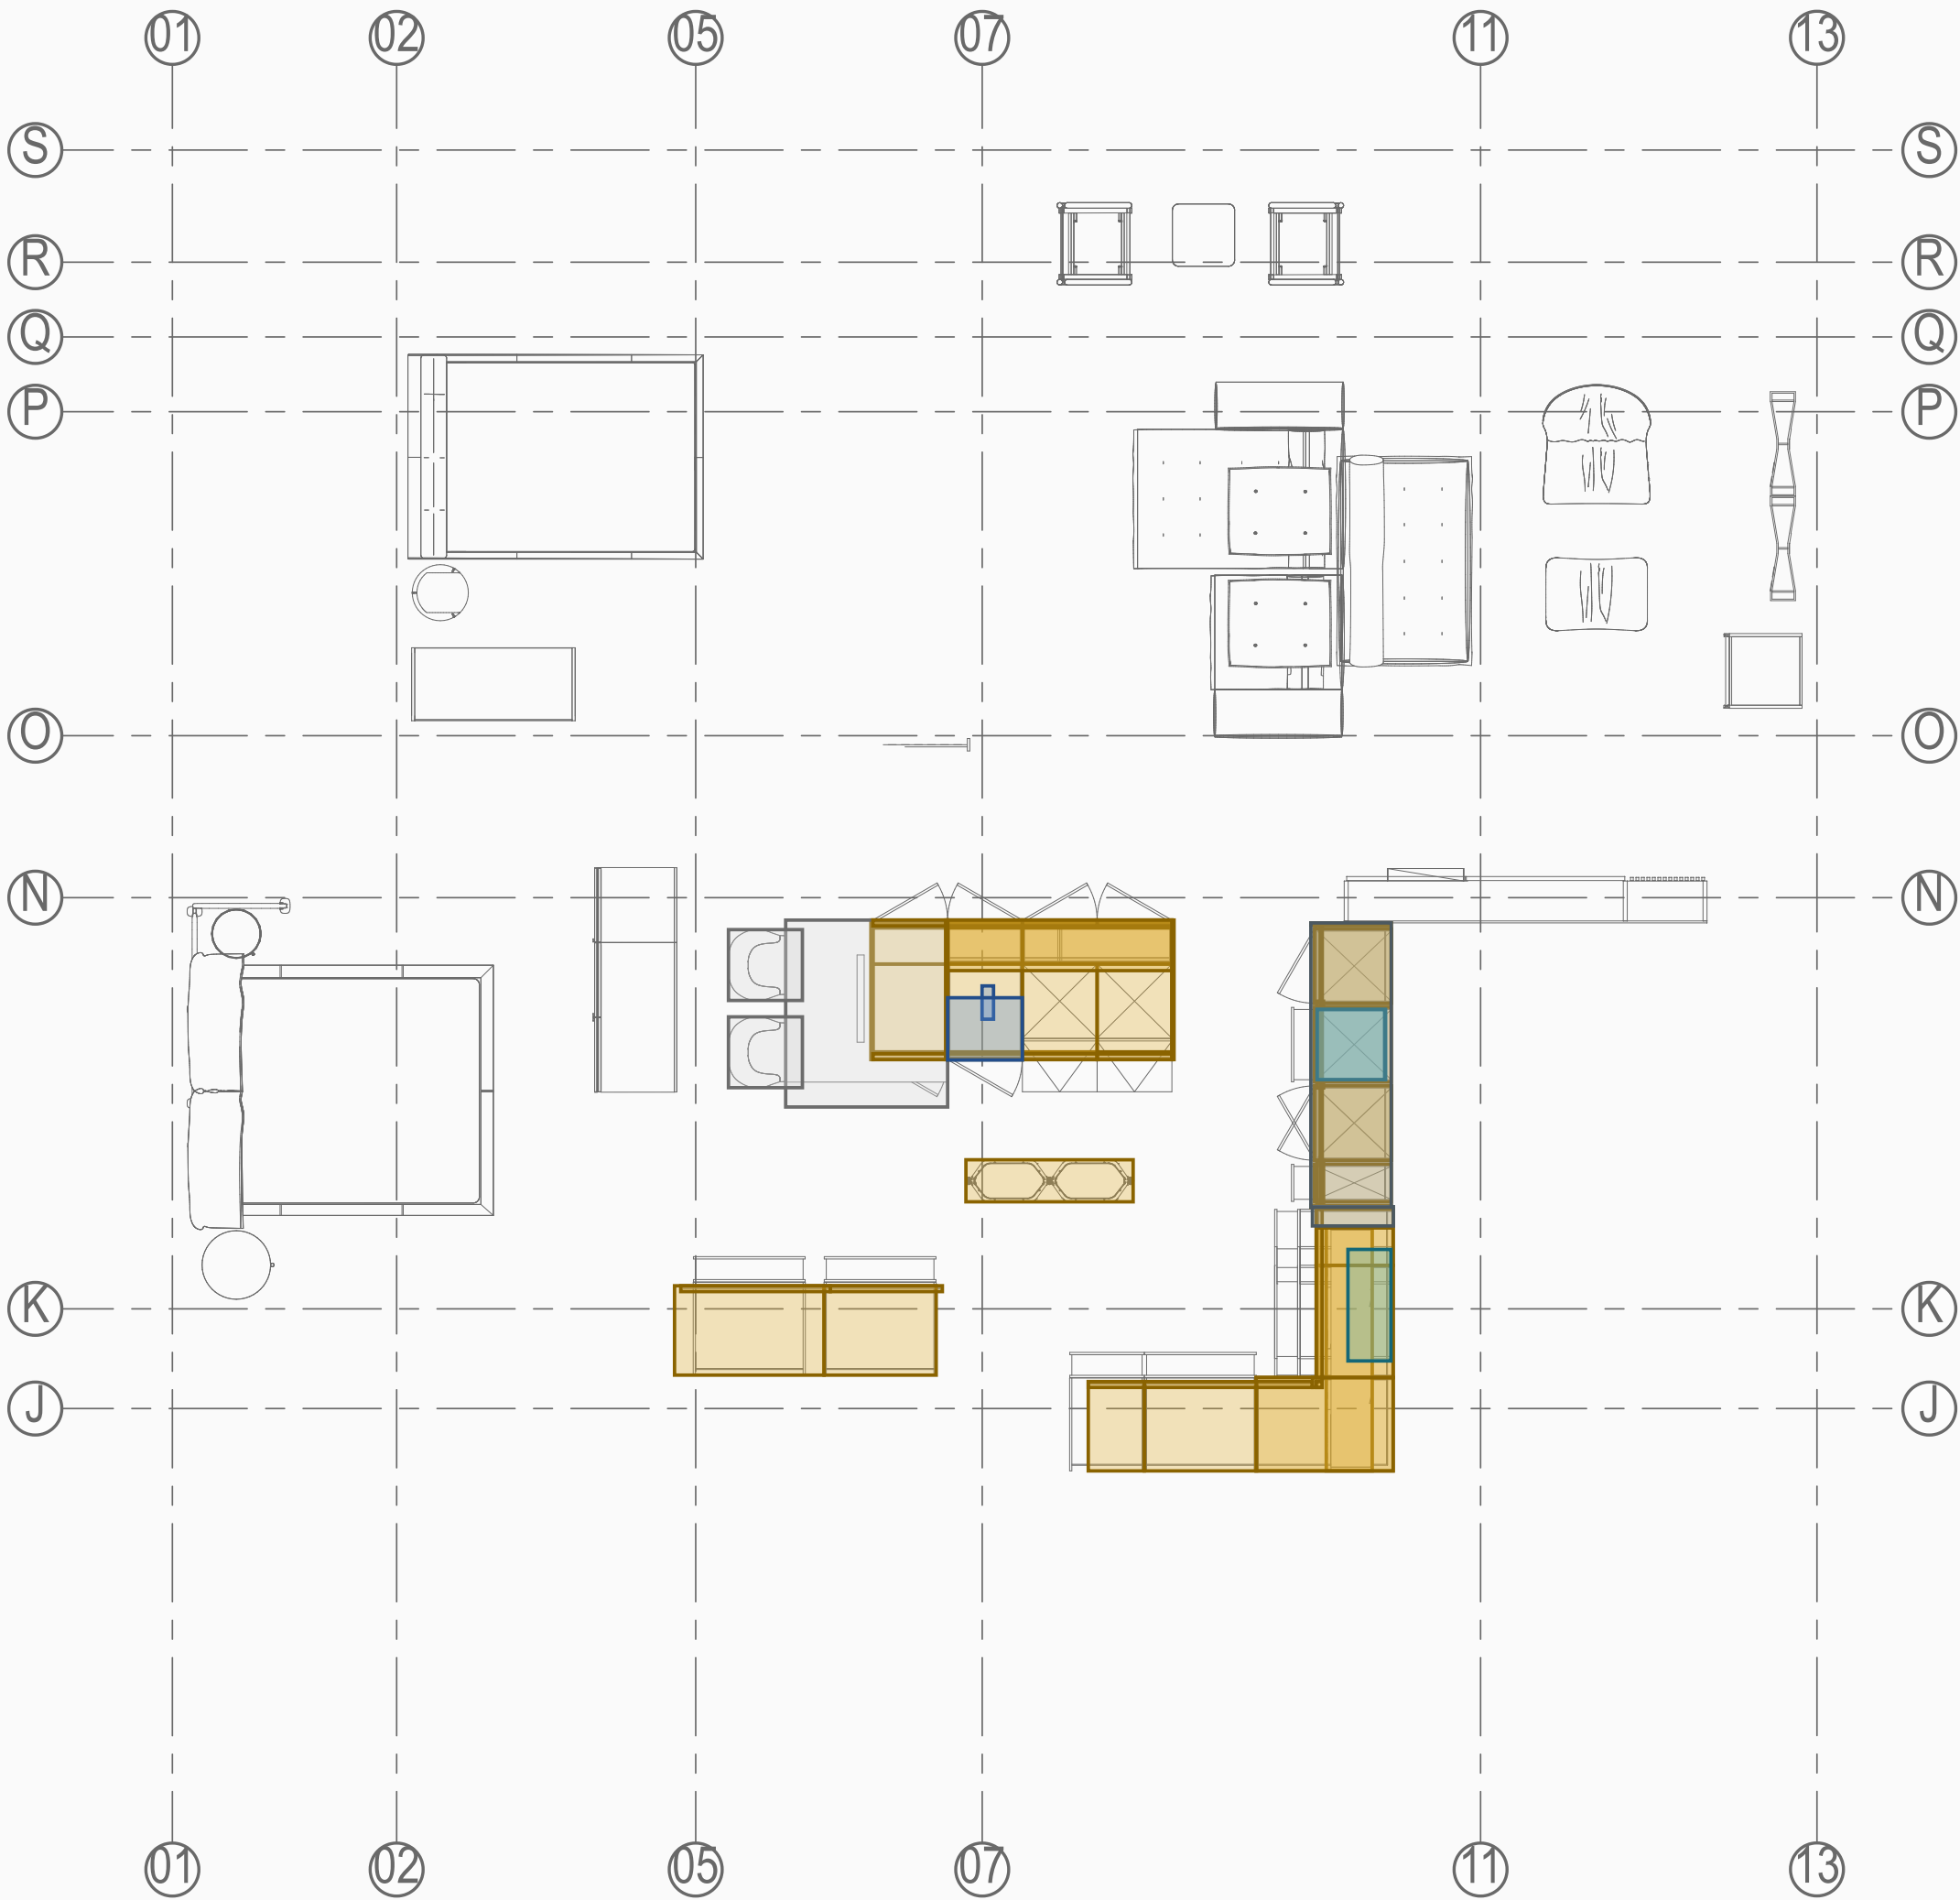

Wall / slab / assembly context Fixed equipment Fixed furniture Sanitary fixture Loose context

Exact GlobalId/object index: pipeline/decisions/int1-existing-review.csv

Base plan retained for context; overlay uses existing world-coordinate bbox only.