


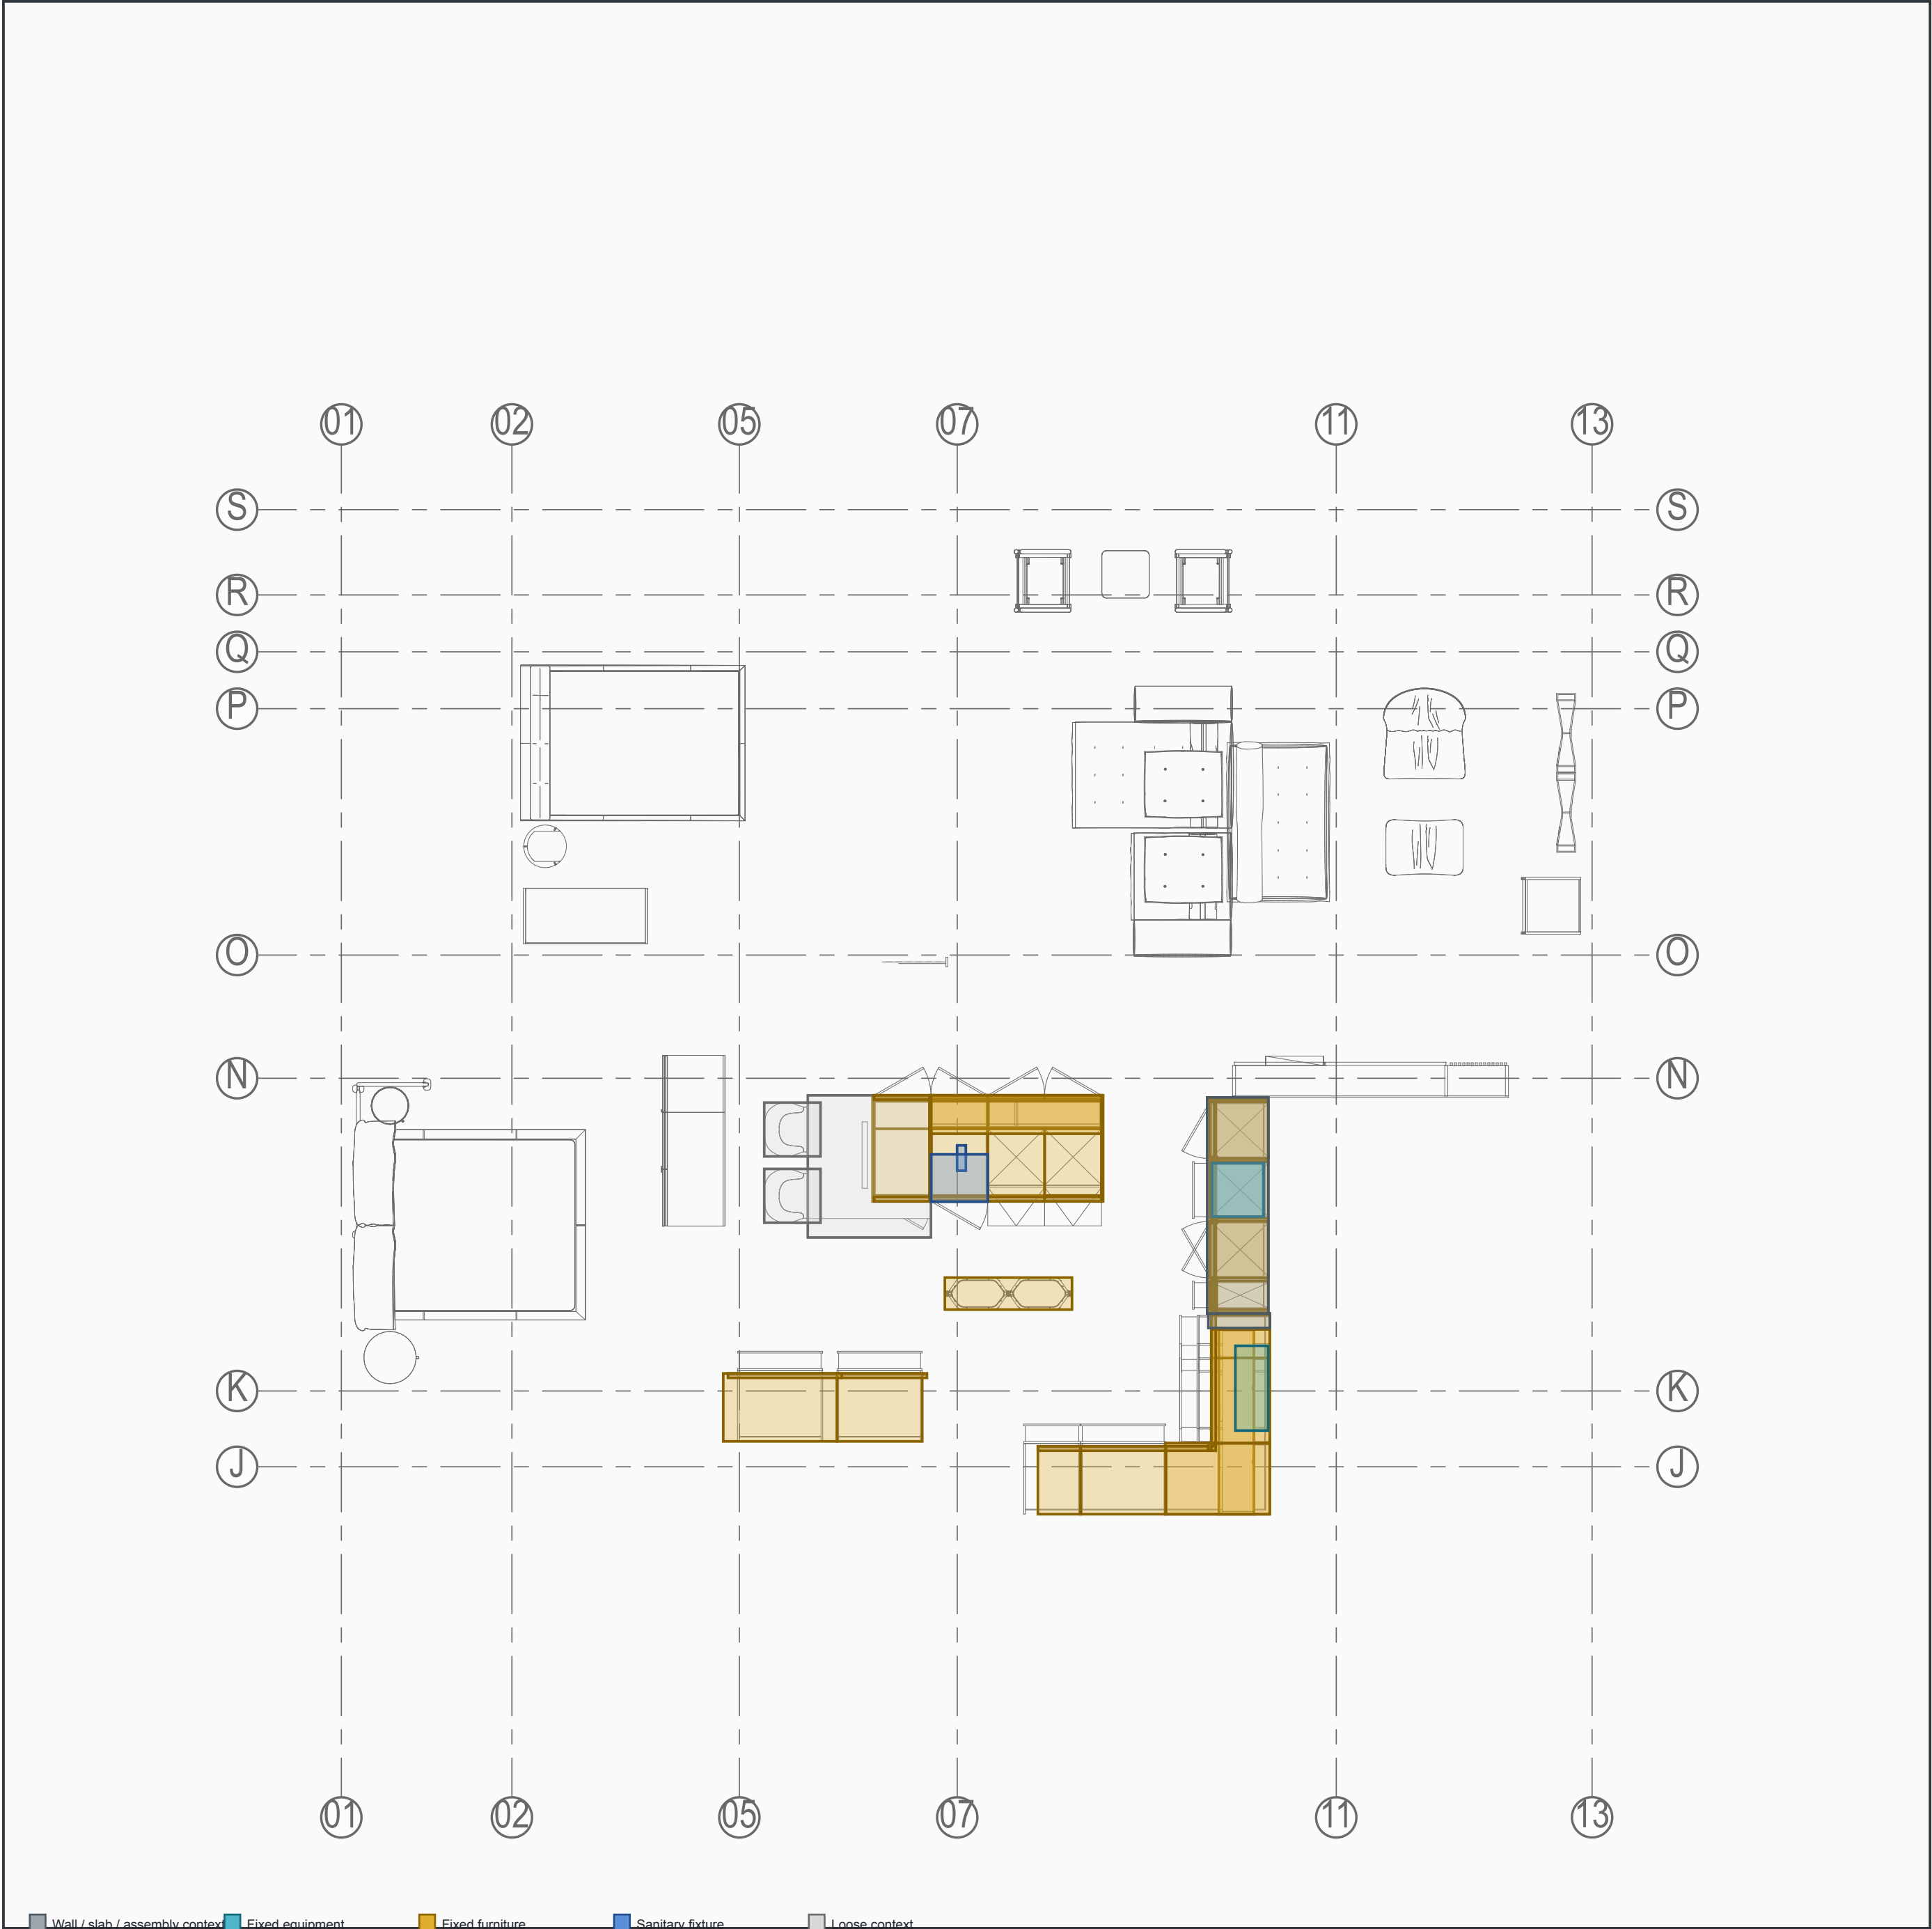

Exact GlobalId/object index: pipeline/decisions/int1-existing-review.csv
Base plan retained for context; overlay uses existing world-coordinate bbox only.

I-501 Kitchen Coordination Candidate

厨房平面与立面协调候选

Status: CANDIDATE / NOT FOR CONSTRUCTION

Existing objects: 70

IFC SHA: 7a50b87e8f48a7c2...

Overlay = world bbox coordination envelope

NOT fabrication / opening / rough-in dimensions

■ Cabinet x1	■ HC02 x1
■ 厨房移门门垛墙 x1	■ HD1200 x2
■ HD01 x1	■ HD450 x3
■ OV01 x1	■ HD600 x8
■ WD01 x1	■ HD900 x3
■ BD600DW x2	■ HL x1
■ BD600P x2	■ HP x1
■ BN1200 x1	■ Libelle x1
■ BN450 x1	■ PAN01 x1
■ BN900 x1	■ POT1200 x1
■ BNW900C x1	■ POT600 x1
■ BS1200P x2	■ SB01 x1
■ BW1200 x1	■ SB02 x1
■ BW450 x1	■ SB03 x2
■ BW900 x2	■ SIS04 x1
■ CAB-A x1	■ SKI03 x1
■ D600P x4	■ SKI04 x2
■ FRE01 x1	■ VVD Island Inner S...
■ FRE02 x1	■ VVD Island worktop...
■ FRI01 x1	■ W06L x1
■ FRI02 x1	■ FAU01 x1
■ H08 x1	■ SIN01 x1
■ H09 x1	■ CHA01 x2
■ HC01 x1	■ TAB01 x1

CONFIRMED · VVD PROJECT MATERIAL DIRECTION

Structure Slate · doors Nebula steel

Thermo oak components · Pewter trims / hood / skirting 60

Top + cook wall backsplash: Travertino titan marble / top 60 mm

Lighting shelves: Thermo oak / thickness 36 mm

Integrated LED extents confirmed; driver / wiring / service pending

Foster 1014 850: 838×500 mm · undermount

Custom sink: width 600 mm confirmed only

VVD example sink W1200 is NOT a project dimension

PENDING: samples / slab layout / cutouts / shelf fixing / sink XYZ

PRODUCT INTERFACES · NO PROJECT XYZ

APP-009 · SJ85ZX26MC · CANDIDATE / NOT PURCHASED

Use: 西厨岛台 · G3/4 cold water · drain Ø38 mm

APP-010 · SJ85ZX26MC · CANDIDATE / NOT PURCHASED

Use: 西厨岛台 · G3/4 cold water · drain Ø38 mm

Niche H780–835 mm · W600–608 mm · D≥550 mm (official product constraint)

BLOCK: rough-in XYZ / valves / hose path / opening position

APP-016 · PROJECT COORDINATION ENVELOPE

Foster bowl 200 + Franke H365 = ≈565 below top

Reserve bottom removal and drain / trap zone

No pull-out storage may enter this envelope

F50 vs Franke: supplier verifies interfaces + quote

SSOT PROJECT DIRECTIONS · DETAIL / SIGN-OFF PENDING

OWNER CONFIRMED · 灶台操作墙台面同材大板；远端墙浅置物架

KNOWN · DETAIL PENDING · 保持正式 IFC 当前相邻布局：600 石材盆 + 洗碗机 + 洗碗机

KNOWN · DETAIL PENDING · 参考 Molteni Eco kits 的盆下抽屉、垃圾桶和清洁用品托盘

KNOWN · DETAIL PENDING · 反灯槽直边铝型材收口；客厅窗帘盒 200 mm；顶天立地酒架上方按最终消

PROJECT DETAIL BASIS · EXTERNAL DIMENSIONS ONLY

600 stone sink: one 600 module; pull-out waste + cleaning storage retained

White remote wall + shallow shelf; removable / backing / clean edge

Ice cream: 500×450×450 clear / 20 kg / 10A; domestic unit only

H70FT + K-D01–04 fixed; site measures size / hardware

BLOCK INT1-BLOCK-001: equipment_installation_drawings

BLOCK INT1-BLOCK-002: gas_meter_site_survey

BLOCK INT1-BLOCK-003: sanitary_rough_in_drawings

BLOCK INT1-BLOCK-004: hardware_motion_envelopes