


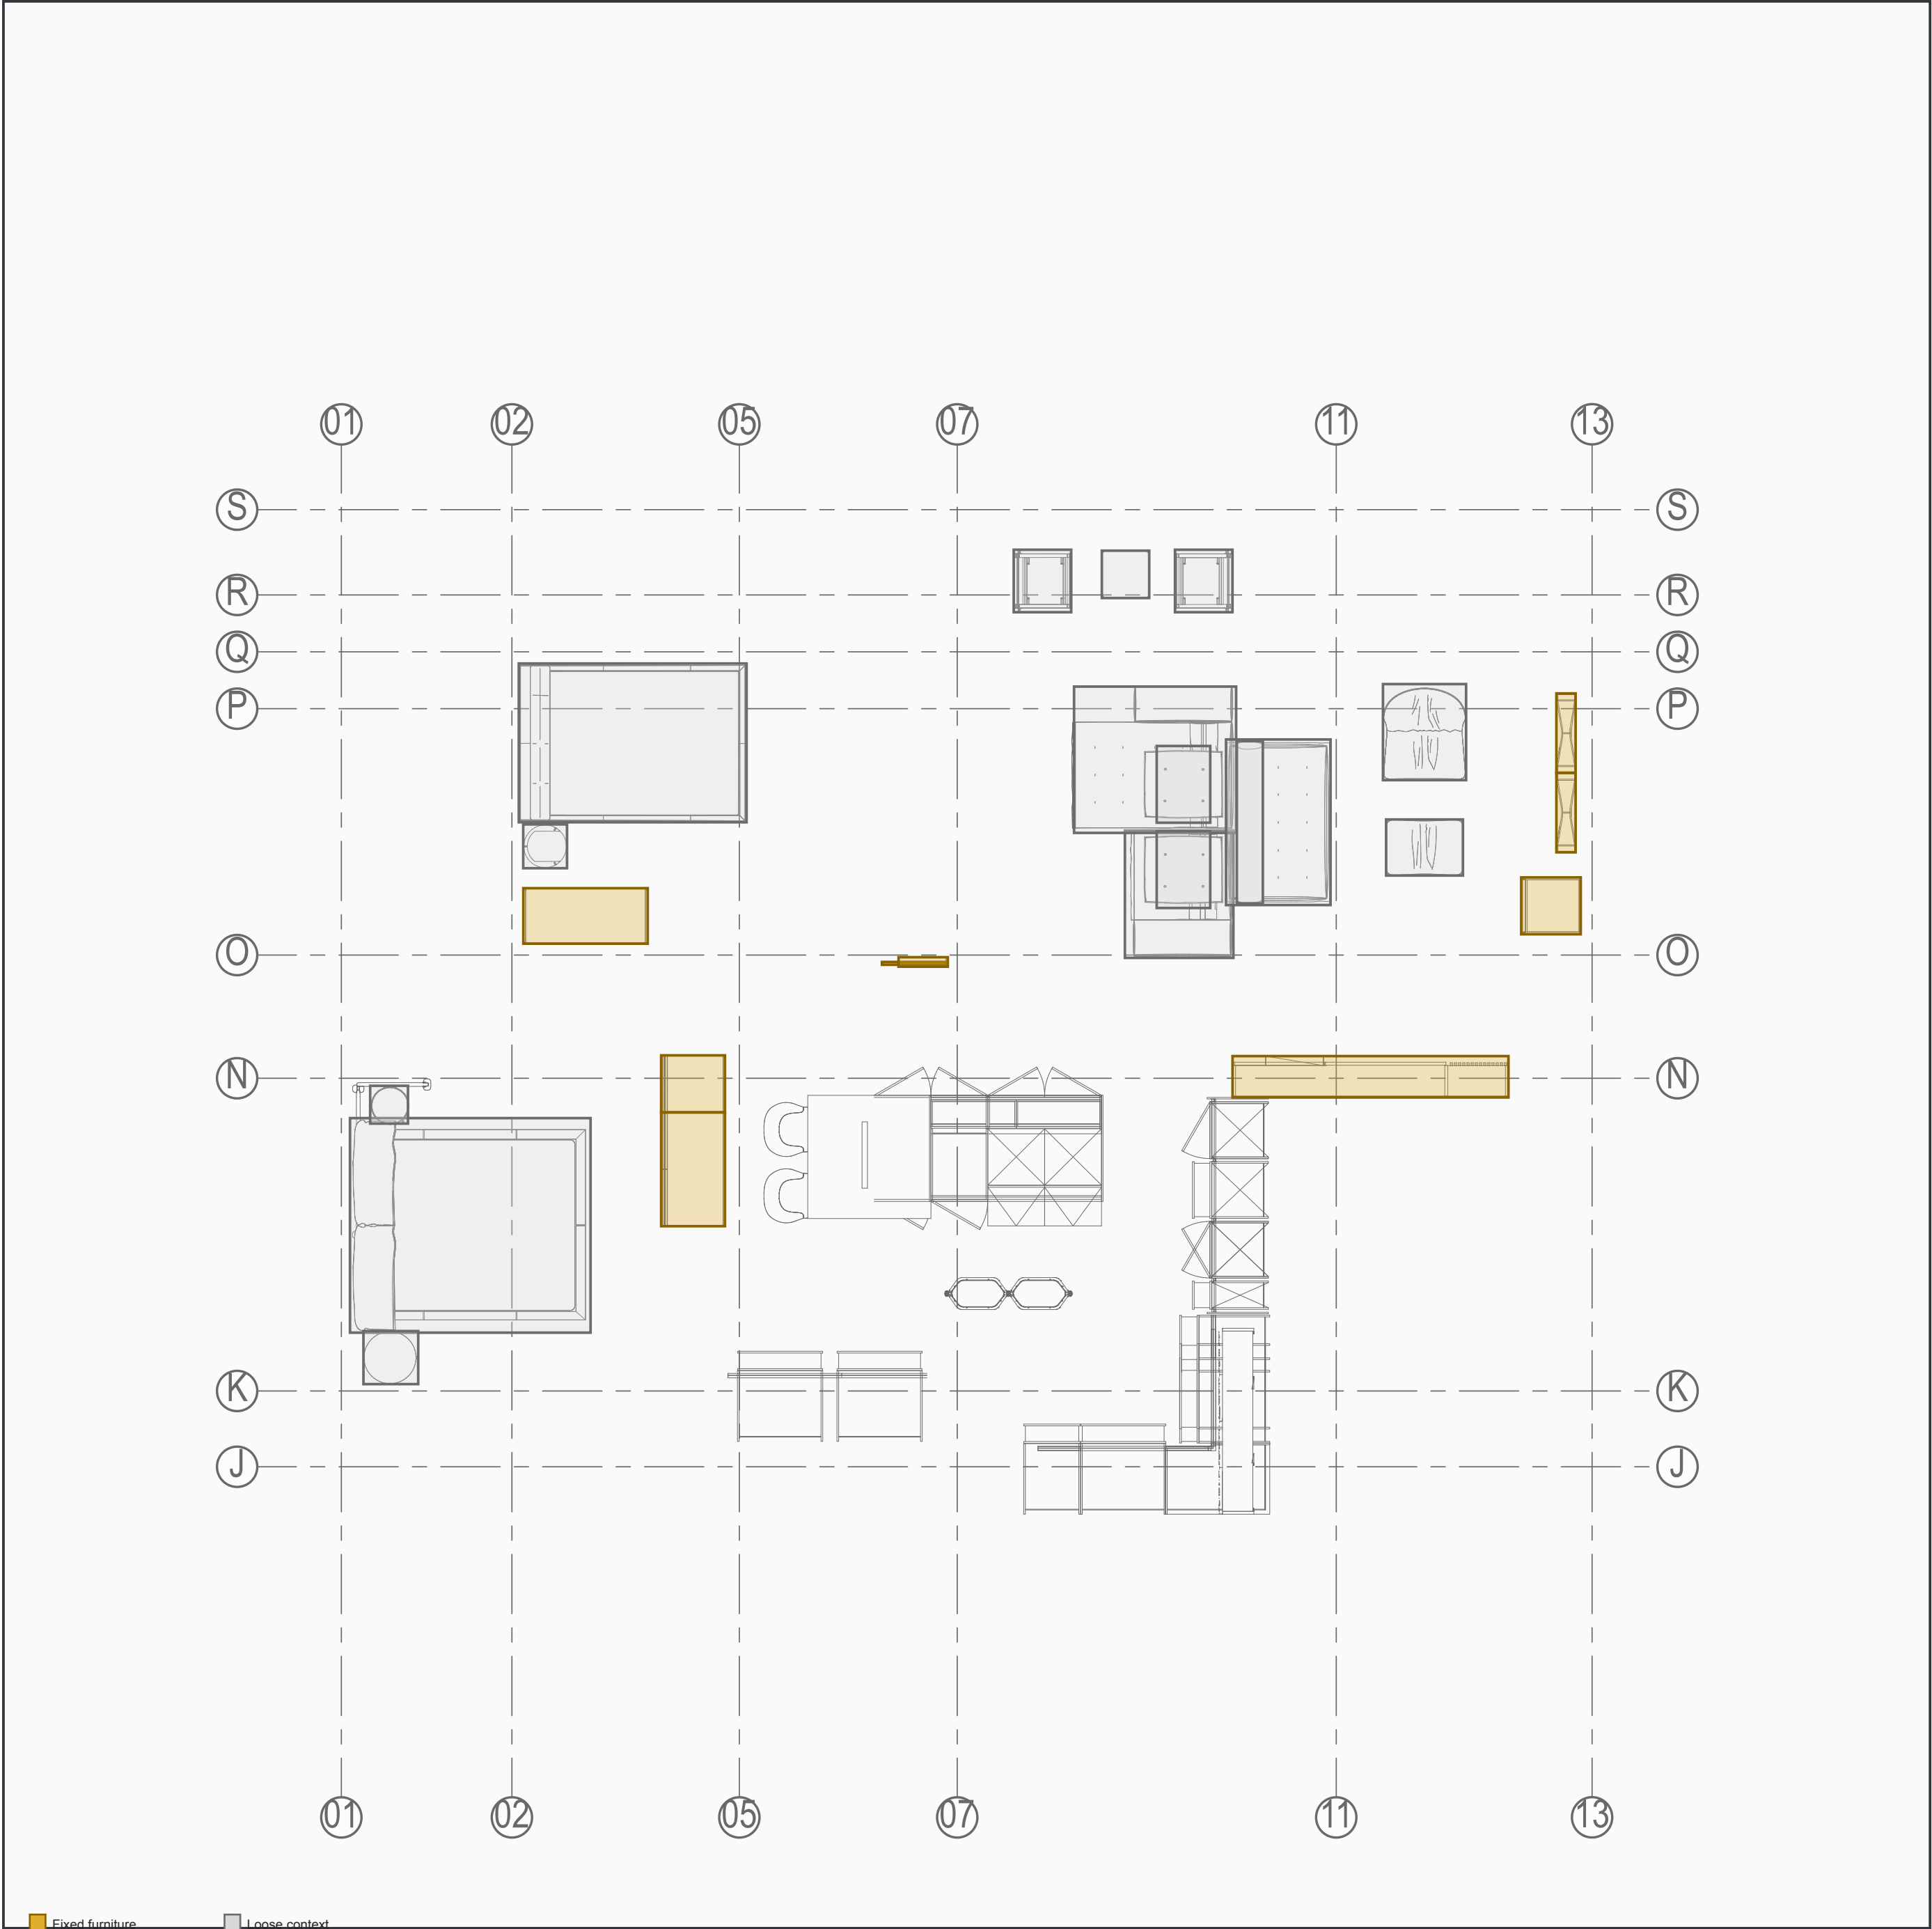

I-504 Fixed Furniture Candidate

其他固定家具平面与立面候选

Status: CANDIDATE / NOT FOR CONSTRUCTION

Existing objects: 25

IFC SHA: 7a50b87e8f48a7c2...

Overlay = world bbox coordination envelope

NOT fabrication / opening / rough-in dimensions

- 505 UP V1.LP.S x1
- GP01 x1
- GP01S x1
- SHE01 x2
- WD01 x1
- WD01L x1
- WD02 x1
- WD03 x1
- BED01 x1
- BED02 x1
- BST01 x1
- BST02 x1
- BST03 x1
- CHA02 x2
- Marilyn 01 x1
- Marilyn 02 x1
- MiamiSoft E07 x1
- MiamiSoft E09 x1
- MiamiSoft F03 x1
- MiamiSoft H01 x2
- MiamiSoft I03 x1
- TAB02 x1

SSOT PROJECT DIRECTIONS · DETAIL / SIGN-OFF PENDING

OWNER CONFIRMED · 墙面同色齐平宽踢脚；上下各约 10 mm 阴影缝；门套、隐形门和柜体边界连续通

KNOWN · DETAIL PENDING · 次卧飘窗落地浅色木；客厅飘窗木盒与大白墙脱缝并齐平墙面

PROJECT NODE · 飘窗木作收口

客厅：木盒与大白墙脱缝，外表面齐平墙面

次卧：浅色木从地面连续落地至飘窗台

基层 / 防潮 / 木饰面 / 弹性边缝 / 窗边密封

不得覆盖窗边排水、渗漏观察或检修

EXTERNAL: 板厚、伸缩、固定、现场 W×H×D、样板

BLOCK INT1-BLOCK-001: equipment_installation_drawings

BLOCK INT1-BLOCK-002: gas_meter_site_survey

BLOCK INT1-BLOCK-003: sanitary_rough_in_drawings

BLOCK INT1-BLOCK-004: hardware_motion_envelopes