

I-502 Bathroom Coordination Candidate

卫生间平面、立面与节点协调候选

Status: CANDIDATE / NOT FOR CONSTRUCTION

Existing objects: 33

IFC SHA: 7a50b87e8f48a7c2...

Overlay = world bbox coordination envelope

NOT fabrication / opening / rough-in dimensions

- CAS130 x2
- WAL170 x2
- HIMA01 x1
- BATH01 x1
- BS01 x1
- FAU02 x1
- Geberit 115.770 x2
- Geberit 146.140 x2
- Geberit 154.154.00 x1
- Geberit 154.154.00.1.C x1
- Geberit 154.154.00.1.F x1
- Geberit 154.446.KS.1 x1
- Geberit Duofix Sigma x2
- Gessi316 54038 x2
- Gessi316 54093 x1
- Gessi316 54145 x1
- Gessi316 54146 x1
- Gessi316 54205 x1
- Gessi316 54294 x1
- PANTA REI x1
- STREET x1
- STREET-H x2
- TRAP01 x1
- JingAn Linear Shower Channel x1
- JingAn Linear Shower Channel Aqura x2

SSOT PROJECT DIRECTIONS · DETAIL / SIGN-OFF PENDING

OWNER CONFIRMED · 台盆左侧全高服务塔；优选面宽 400 mm，可调 350–450 mm；深 250–280 mm...

OWNER CONFIRMED · 指定主页商家；水母地漏/中央集水器+托克乐思网+线性地漏排水渠

PROJECT BATHROOM BASIS · NO VENDOR RE-LAYOUT

Guest mirror cabinet: 400 baseline; full-height mirrored front

Keep basin / service tower / door opening / internal service route

Master Street + guest Sorgente locations and service relations fixed

Fabricator supplies exact L×D×H / bowl / fixing / drain shop drawing

Custom drains stay in project wet zones; vendor cannot move fixtures

Vendor returns length / outlet / flow / water seal / flange interfaces


Geberit hidden centres remain unknown until exact official install drawing

BLOCK INT1-BLOCK-001: equipment_installation_drawings

BLOCK INT1-BLOCK-002: gas_meter_site_survey

BLOCK INT1-BLOCK-003: sanitary_rough_in_drawings

BLOCK INT1-BLOCK-004: hardware_motion_envelopes

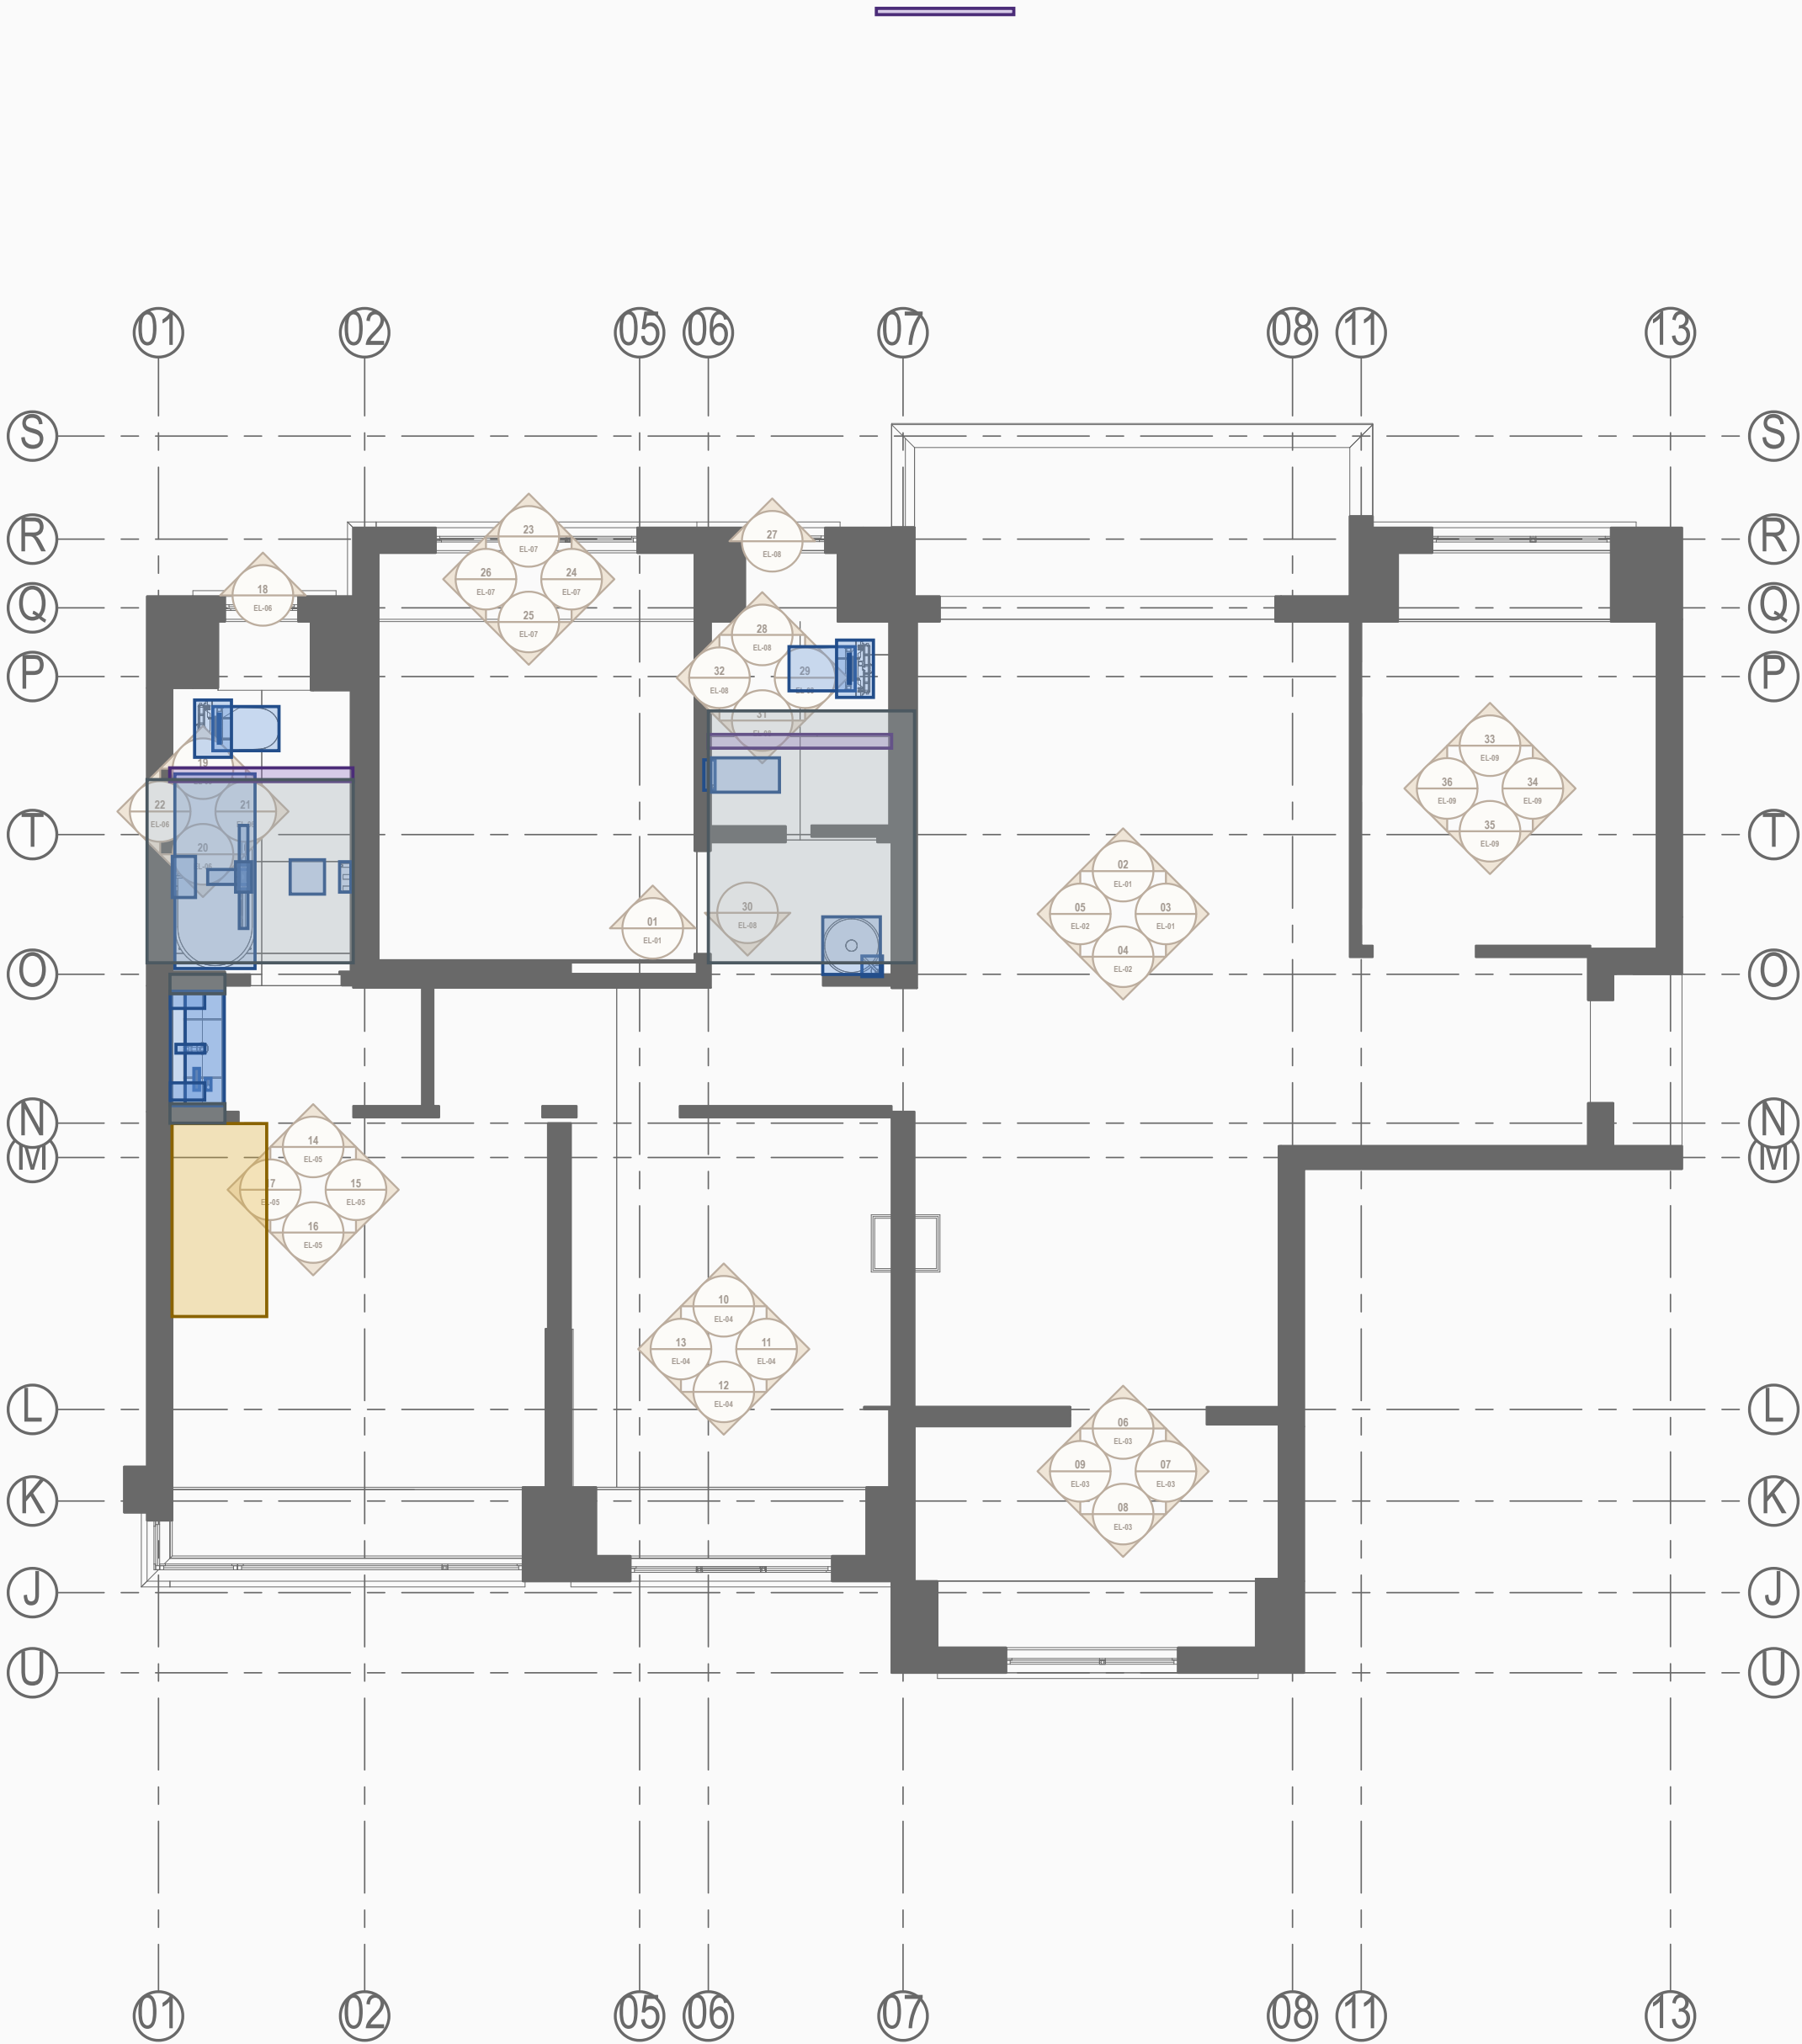

Exact GlobalId/object index: pipeline/decisions/int1-existing-review.csv

Base plan retained for context; overlay uses existing world-coordinate bbox only.